


Floor FC-1

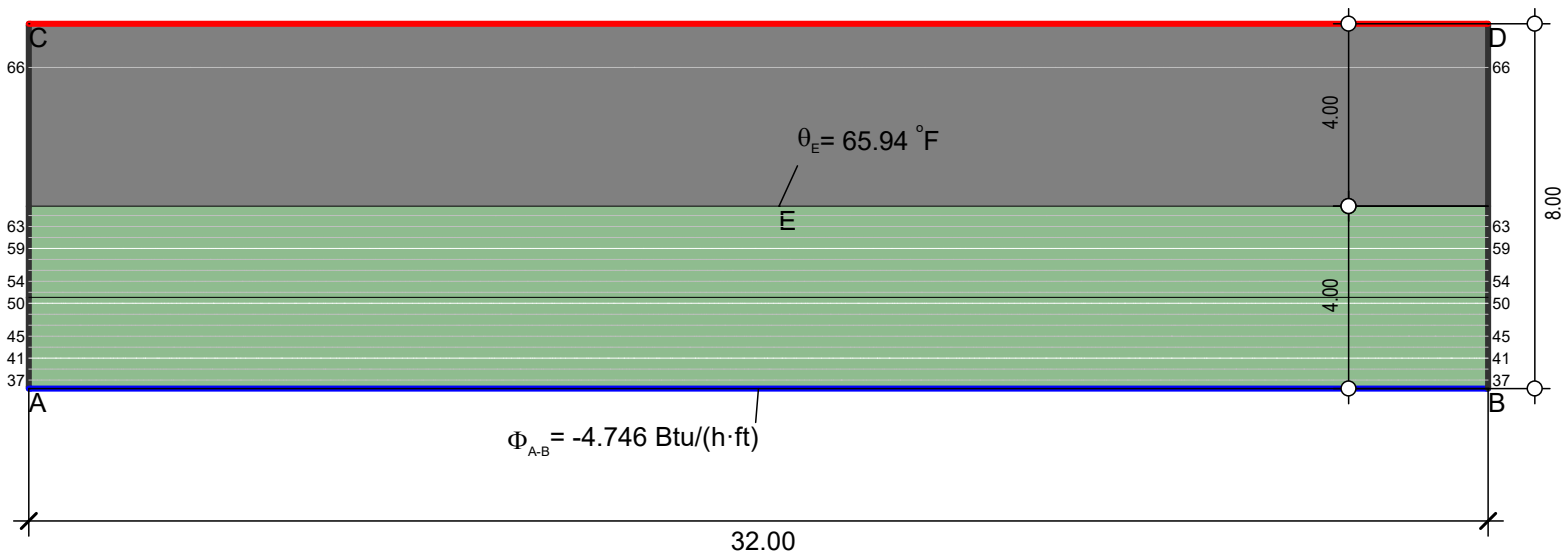

$$U_{eq\ A-B} = \frac{4.746}{32.4 \cdot 2.667} = 0.0549\ Btu/(h \cdot ft^2 \cdot F) = R-18.2149$$

Boundary Condition	$\theta [^{\circ}F]$	$h [Btu/(h \cdot ft^2 \cdot F)]$
Exterior, Westerly 90d Avg	35.600	4.403
Interior, heat flux, downwards	68.000	1.036
Symmetry/Model section		

Material	$\lambda [Btu/(h \cdot ft \cdot F)]$	ϵ
Concrete (Heavily Reinforced) [R-0.05/in]	1.733	0.900
Roxul Comforboard 80 [R-4.2/in]	0.020	0.900