


Wall EW-4

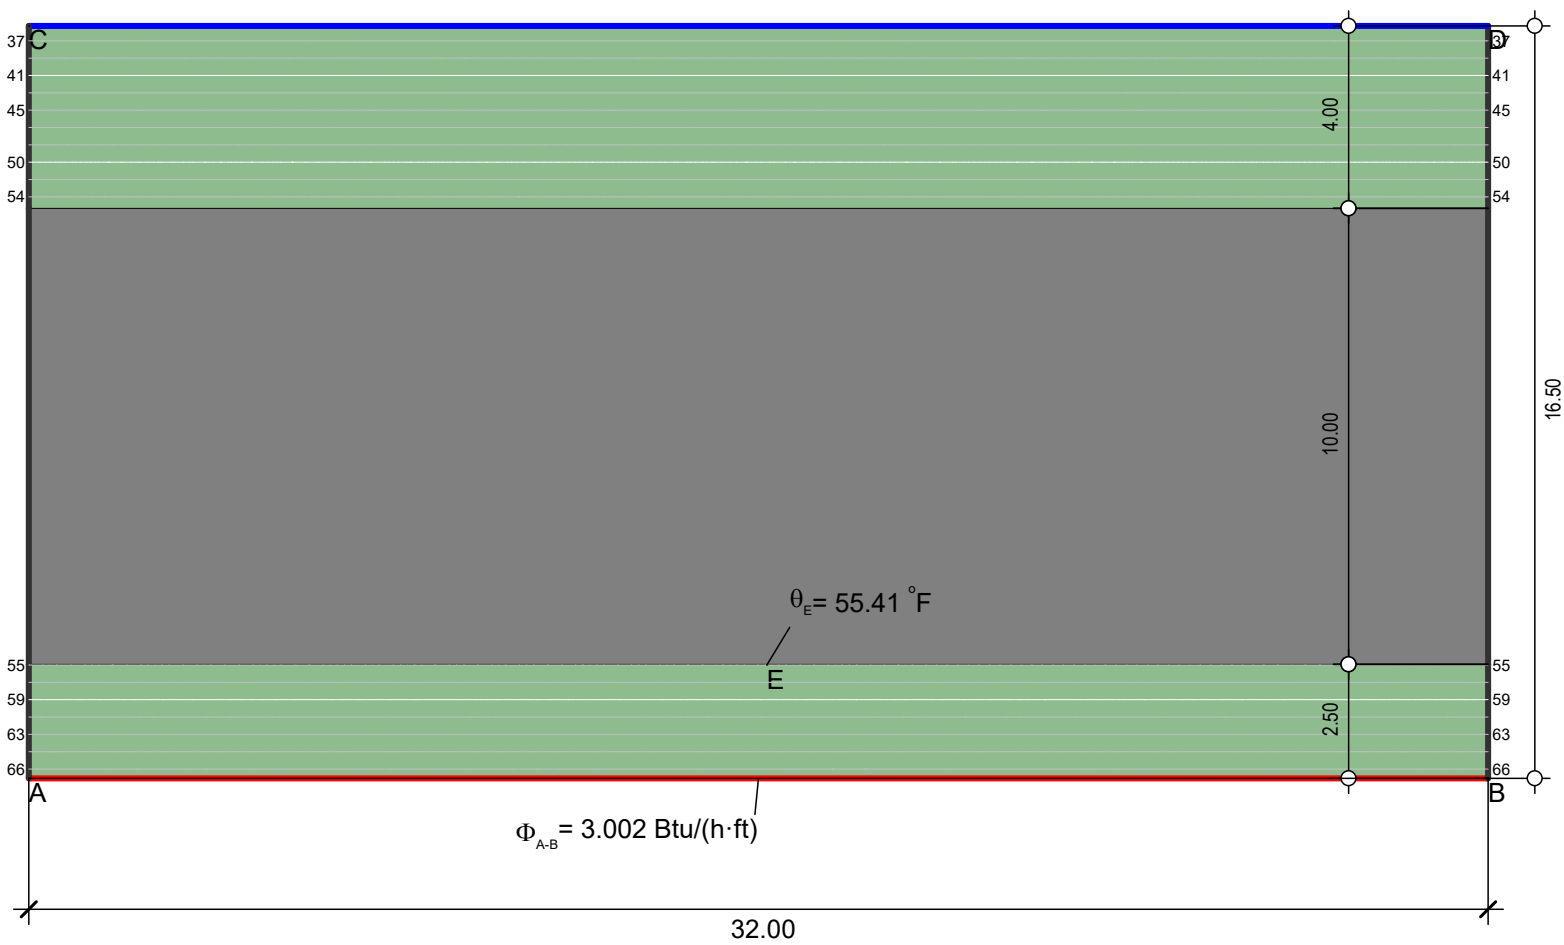

$$U_{eq \text{ A-B}} = \frac{3.002}{32.4 \cdot 2.667} = 0.0347 \text{ Btu}/(\text{h}\cdot\text{ft}^2\cdot\text{F}) = R-28.8184$$

Boundary Condition	$\theta [^\circ\text{F}]$	$h [\text{Btu}/(\text{h}\cdot\text{ft}^2\cdot\text{F})]$
Exterior, Westerly 90d Avg	35.600	4.403
Interior, normal, horizontal	68.000	1.355
Symmetry/Model section		

Material	$\lambda [\text{Btu}/(\text{h}\cdot\text{ft}\cdot\text{F})]$	ε
Concrete (Heavily Reinforced) [R-0.05/in]	1.733	0.900
Roxul Comforboard 80 [R-4.2/in]	0.020	0.900